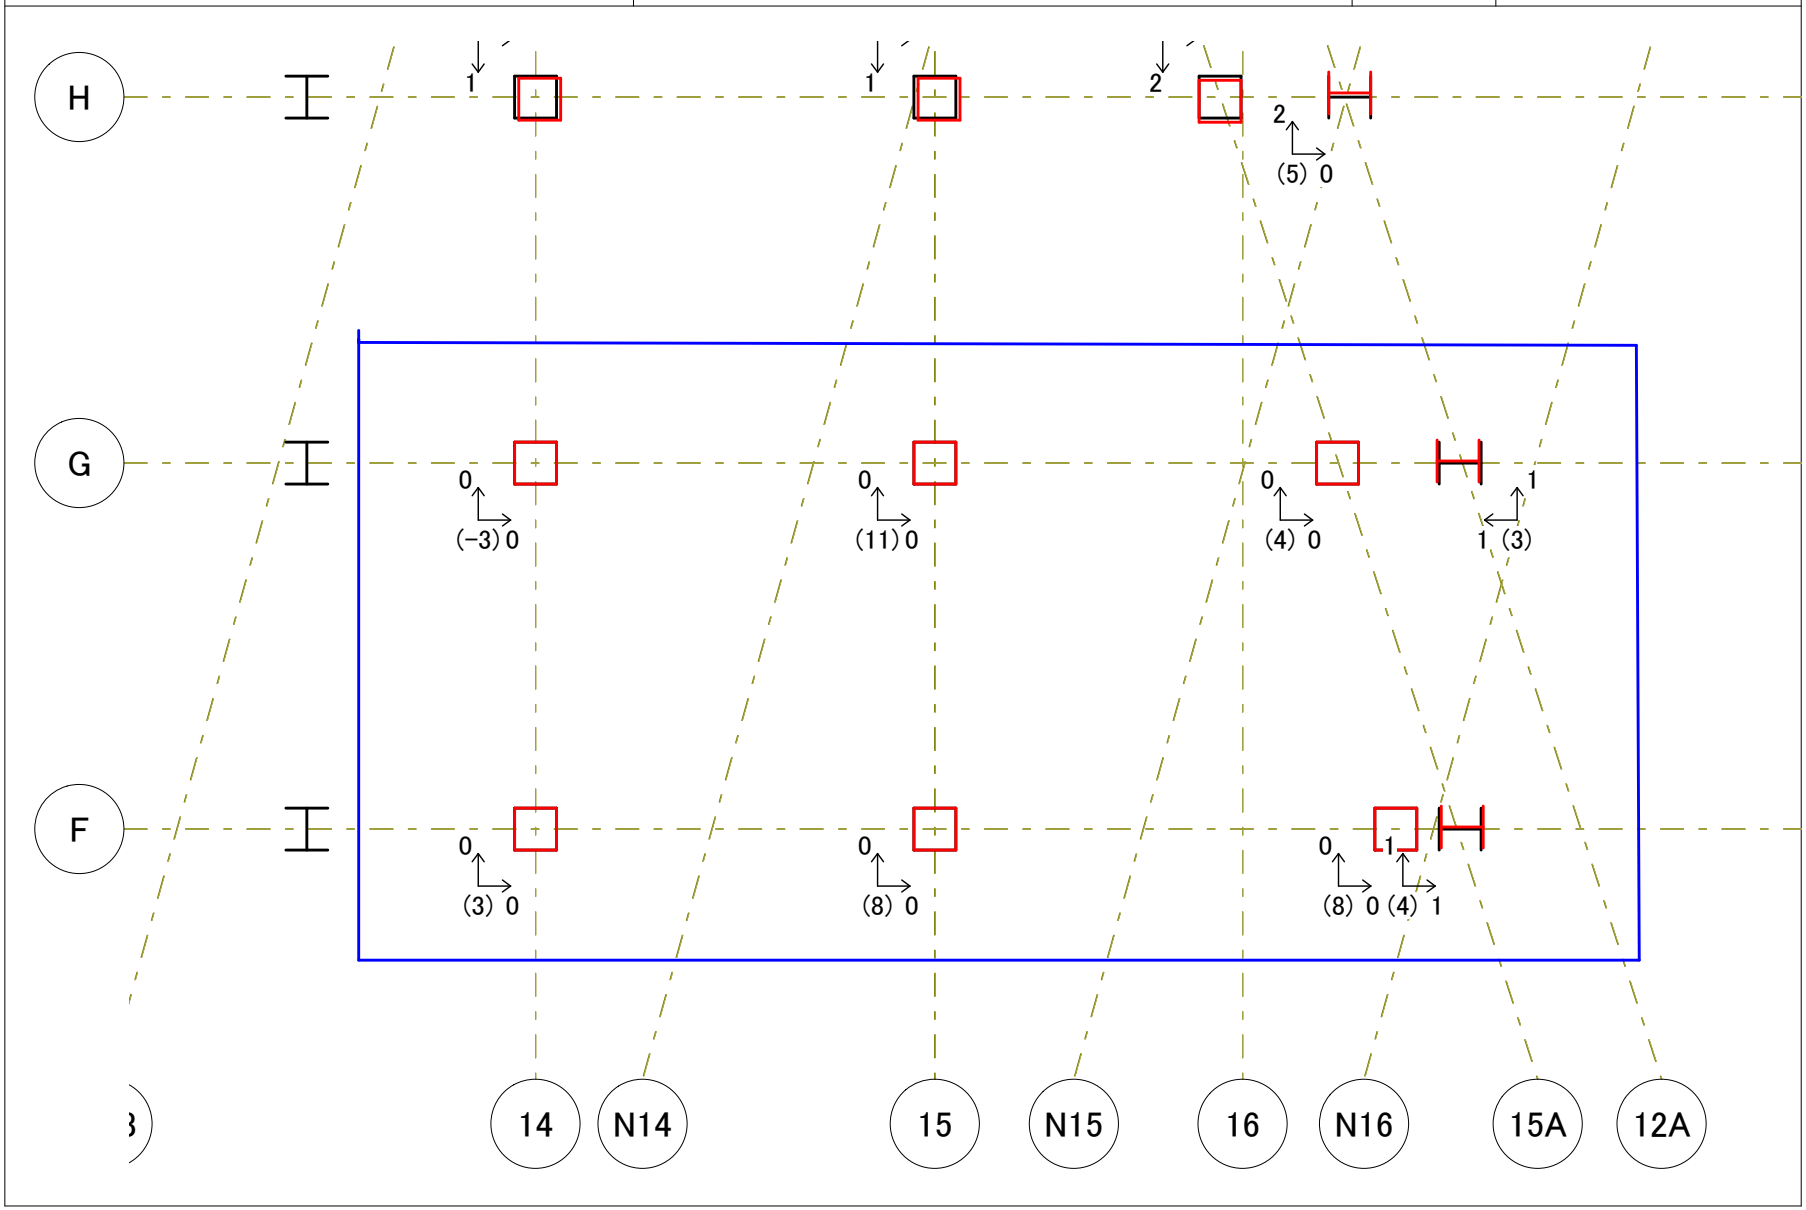梅田1丁目1番地計画作業所	0.5節 平面図　建て方完了後	計測日	2015/08/22
	（基本データとの比較）　　0節下部柱建方完了後実測結果	計測者	KANGI 竹下